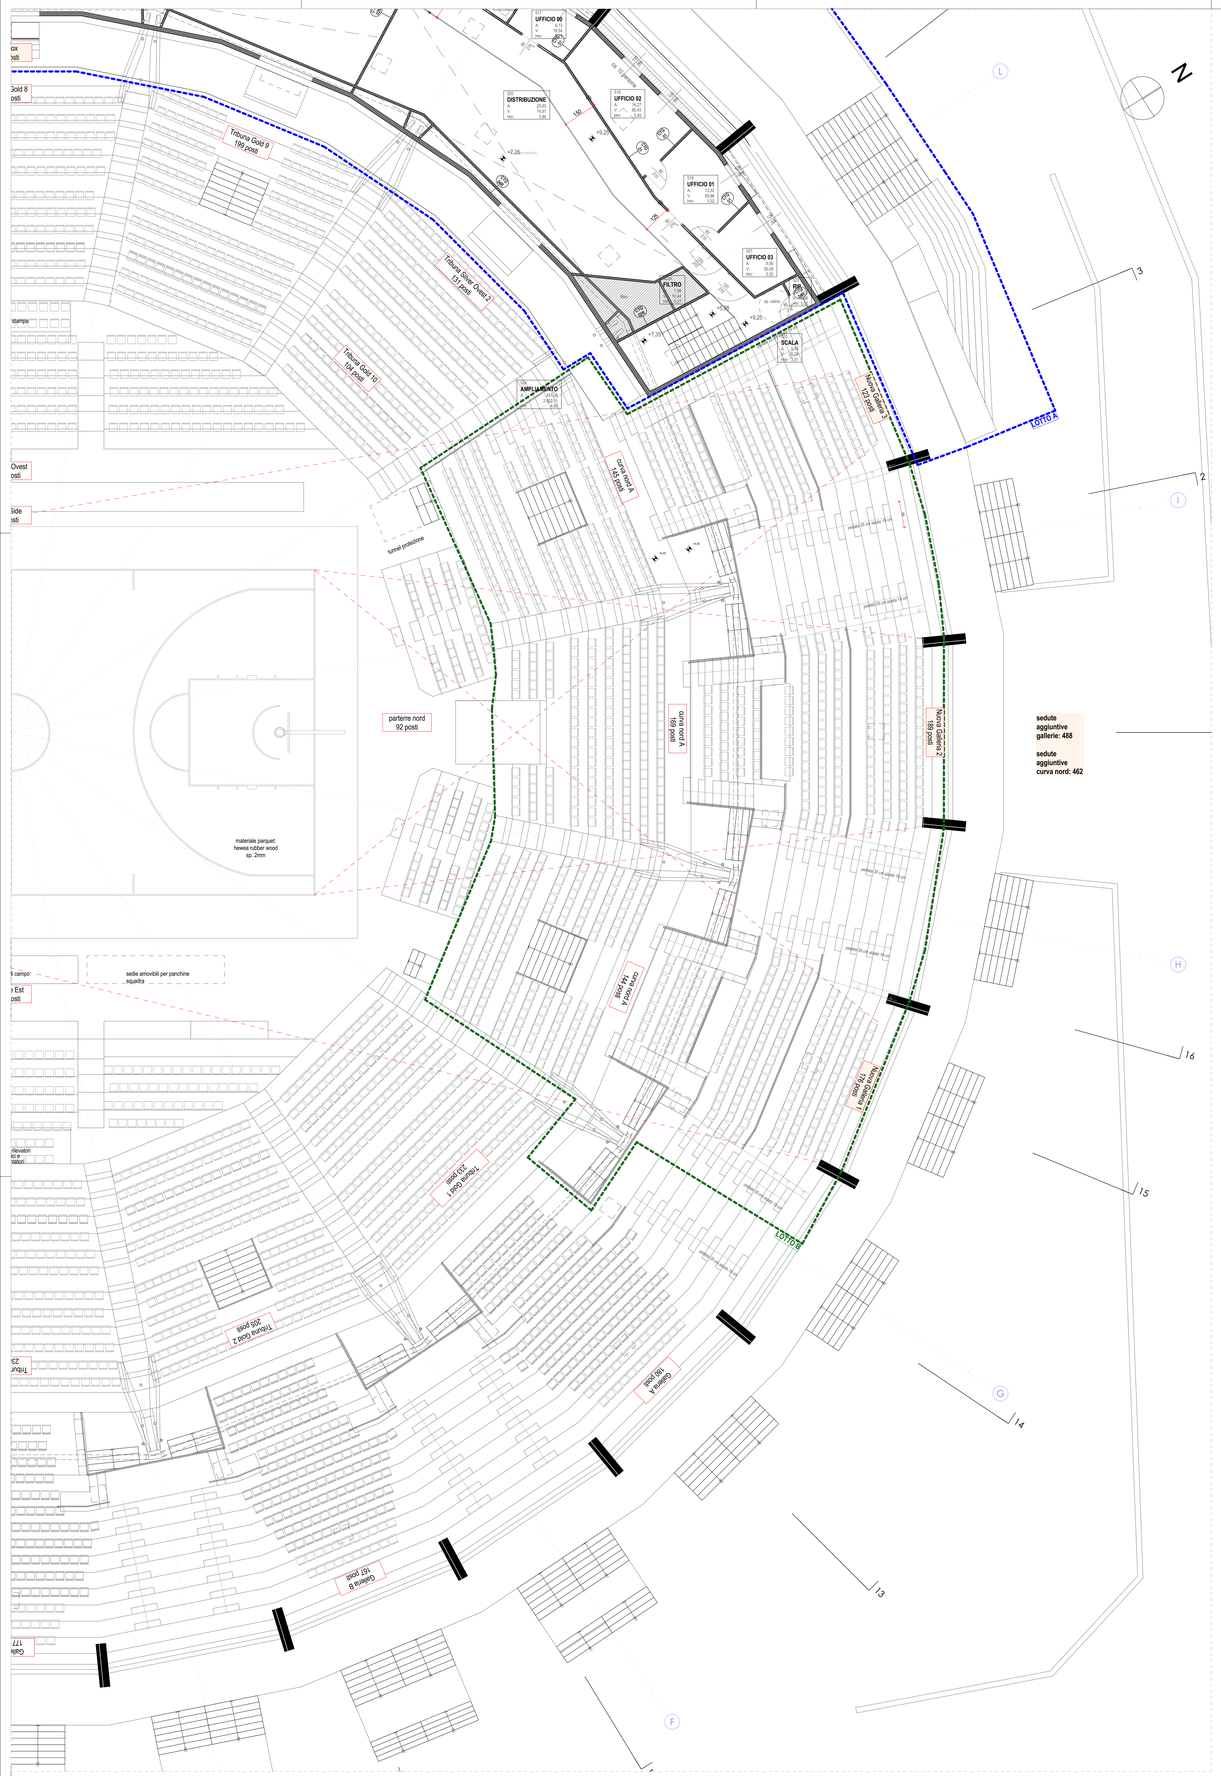

L_03P +9,25 1:100

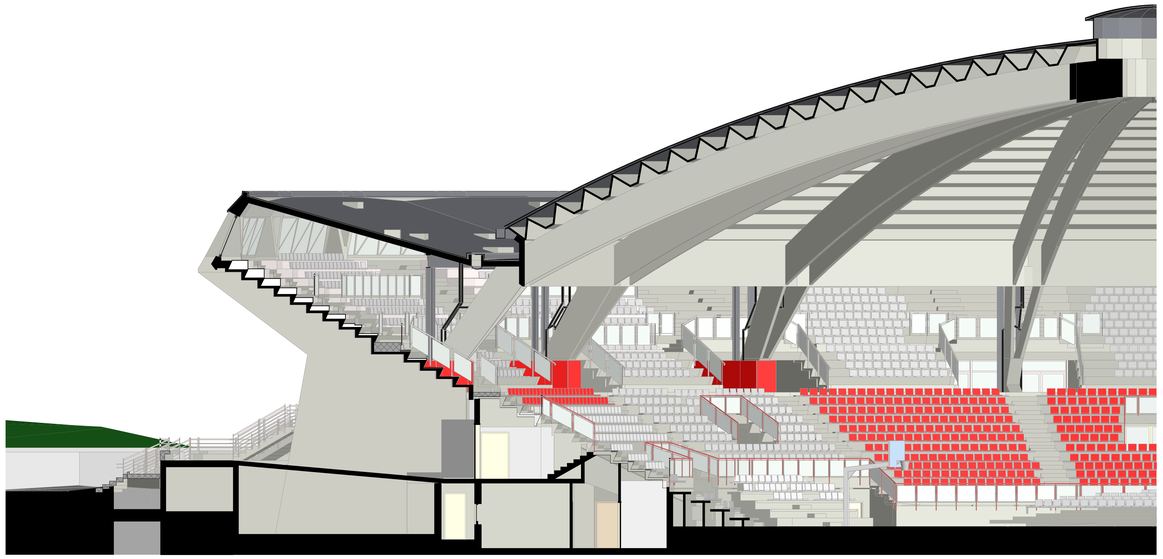

3 Sezione 1:100

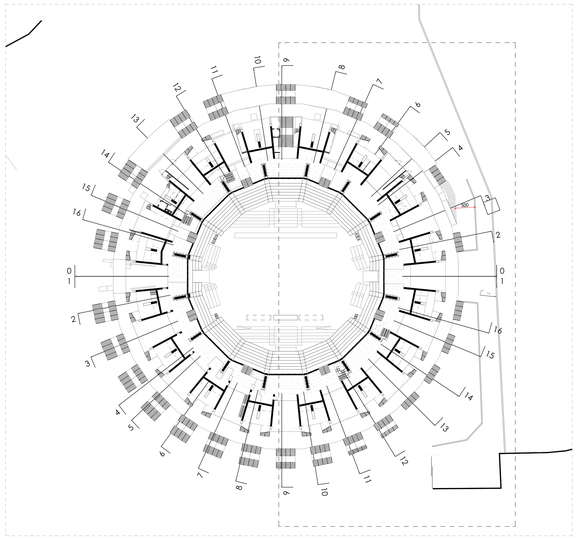

KEYPLAN SDP

LEGENDA MURATURE

CTG 01
1 cm. Lastra cartongesso tipo standard
1 cm. Lastra cartongesso tipo standard
1 cm. Aria / Ventilazione
4 cm. Pannelli di lana di roccia
1 cm. Lastra cartongesso tipo standard
1 cm. Lastra cartongesso tipo standard

CTG 04/5
1 cm. Lastra cartongesso resistente al fuoco
1 cm. Lastra cartongesso resistente al fuoco
4 cm. Pannelli di lana di roccia
4 cm. Pannelli di lana di roccia
1 cm. Lastra cartongesso resistente al fuoco
1 cm. Lastra cartongesso resistente al fuoco

CTG 06
1 cm. Lastra cartongesso resistente al fuoco
1 cm. Lastra cartongesso resistente al fuoco
1 cm. Aria / ventilazione
4 cm. Pannelli di lana di roccia
1 cm. Lastra cartongesso resistente al fuoco
1 cm. Lastra cartongesso resistente al fuoco

CTG 09/A
1 cm. Lastra cartongesso tipo standard
1 cm. Lastra cartongesso ad elevata resistenza
4 cm. Pannelli di lana di roccia
4 cm. Pannelli di lana di roccia
1 cm. Lastra cartongesso resistente all'acqua
1 cm. Lastra cartongesso resistente all'acqua

CTG 03
1 cm. Lastra cartongesso tipo standard
1 cm. Lastra cartongesso ad elevata resistenza
4 cm. Pannelli di lana di roccia
4 cm. Pannelli di lana di roccia
1 cm. Lastra cartongesso resistente all'acqua
1 cm. Lastra cartongesso resistente all'acqua

STR 03
25 cm. CLS per travi pilastri scale C28/30
Rivestimento in lamiera forata

LEGENDA SOLAI

SOL 01 / CA
5 cm. Isolamento - EPS
30 cm. Calcestruzzo solaio - EPS travetti CA passo 80
5 cm. CLS per tree pilastri scale C28/30

COP 01
20 cm. Isolamento - EPS
2 cm. Guaina impermeabile - alta riflettanza solare

COP / SIP
25 cm. CLS prefabbricato solaio
5 cm. Alluminio

COP 02 / CARP
5 cm. Pannelli truciolato
20 cm. Isolamento - EPS
5 cm. Aria / Ventilazione
5 cm. Alluminio

LEGENDA SIMBOLOGIA

- CTG 01 — ETICHETTA MURATURE
- C7 — N. SEZIONE
- SDP +0.00 — QUOTA PAVIMENTO
- NON ACCESSIBILE
- LOTTO A — MUSEO - UFFICI BAR RISTORO
- LOTTO B — AMPLIAMENTO PALAZZETTO

CONVENZIONE DISEGNO

ESISTENTE | PROGETTO

PROGETTO DEFINITIVO

PROGETTO ARCHITETTONICO

PROGETTISTA ARCHITETTONICO
Arch. Elena Brusa Pasquè
Studio Associato Brusa Pasquè
via Rainoldi 27 - 21100 Varese (VA)
tel: 0332 236317 mail: info@brusapasque.it

ORDINE DEGLI ARCHITETTI PIANIFICATORI PAESAGGISTI E CONSERVATORI DELLA PROVINCIA DI VARESE
Brusa Pasquè Elena
573

ING. STRUTTURISTA
Ing. Riccardo Aceti
Studio Aceti - Ingegneria strutturale
via Pasubio 26, 21100 Varese (VA)

ORDINE DEGLI INGEGNERI DELLA PROVINCIA DI VARESE
Dott. Ing. RICCARDO ACETI n° 2197

PROGETTISTA IMPIANTI
SEINGIM - engineering & management
Via Angelo Scarsellini, 14, - 20161 Milano (MI)

ORDINE INGEGNERI PROVINCIA DI MILANO
N. 4347

COMMITTENTE

Pallacanestro Varese
Piazzale Gramsci c/o Enerxenia Arena
(Gestore del Palazzetto "Lino Oldrini" di Varese di proprietà comunale)

LUOGO OGGETTO DI INTERVENTO:

RIQUALIFICAZIONE E COMPLETAMENTO PALAZZETTO DELLO SPORT E REALIZZAZIONE DEL MUSEO DEL BASKET
Palazzetto dello Sport, Piazza Antonio Gramsci, Varese

CUP: B37H21001160002

TIPOLOGIA DI INTERVENTO

RISTRUTTURAZIONE EDILIZIA

REV.	DATA	DESCRIZIONE	DISEGNATO	VERIFICATO	APPROVATO
1	05/10/2021	PROGETTO DEFINITIVO	MZ	EBP	EBP
0	15/07/2021	PROGETTO DEFINITIVO	MZ	EBP	EBP

NOME FILE	
DATA DI STAMPA	
STILE DI STAMPA	
NOME LAYOUT	

TITOLO
SDP PIANTA | PIANO +9,25

SCALA
1:100

TAVOLA
NE - SDP - 05