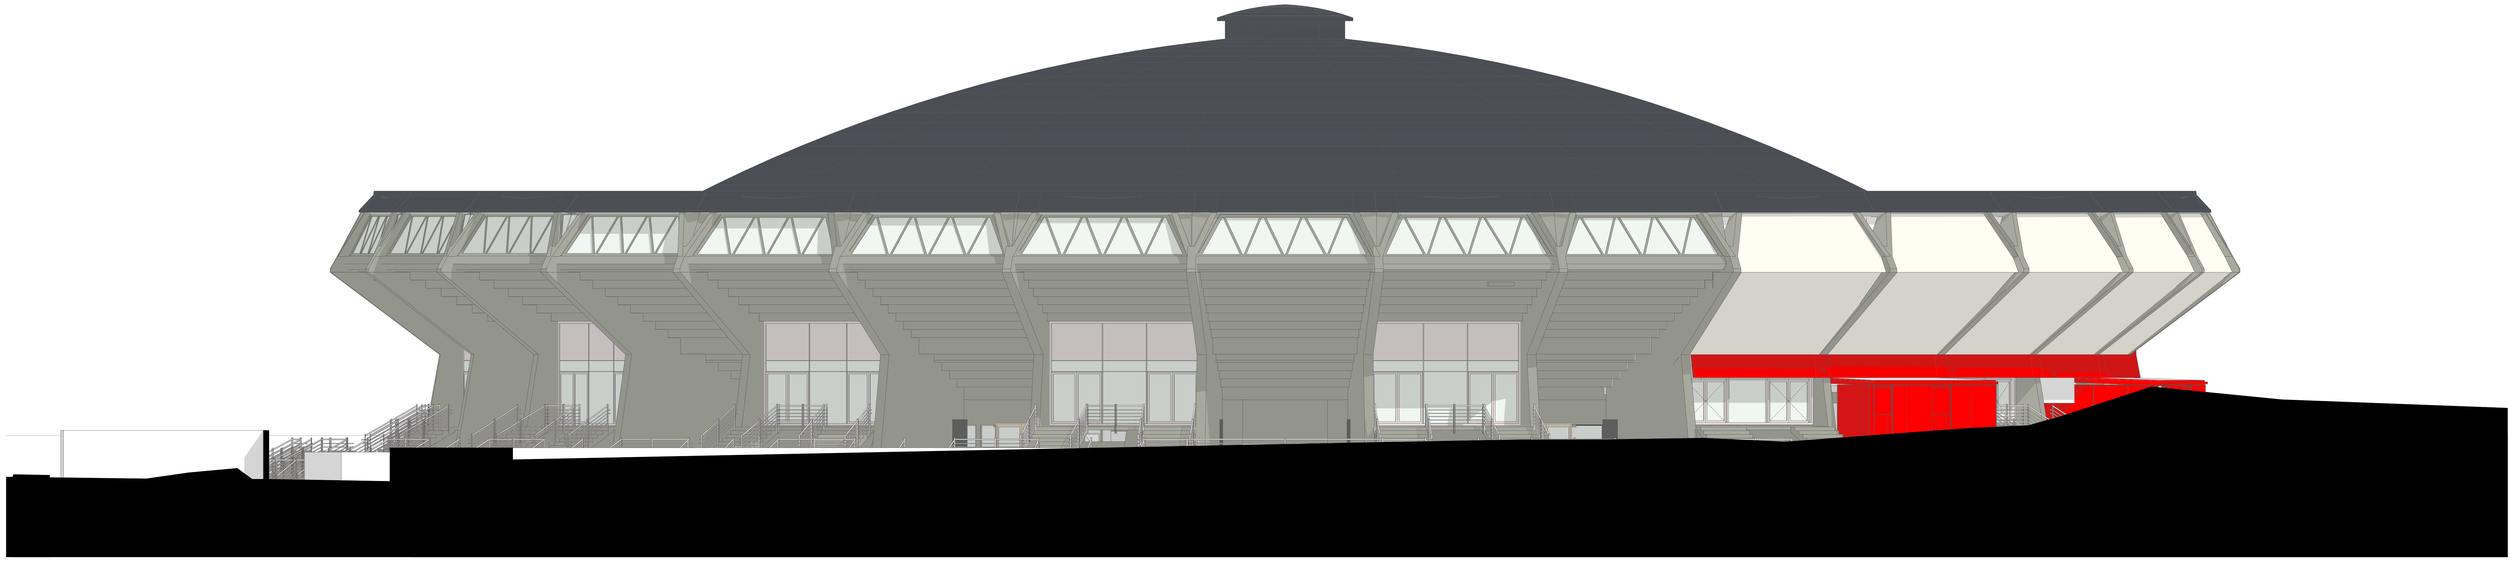

02 Prospetto NORD_EST 1:100

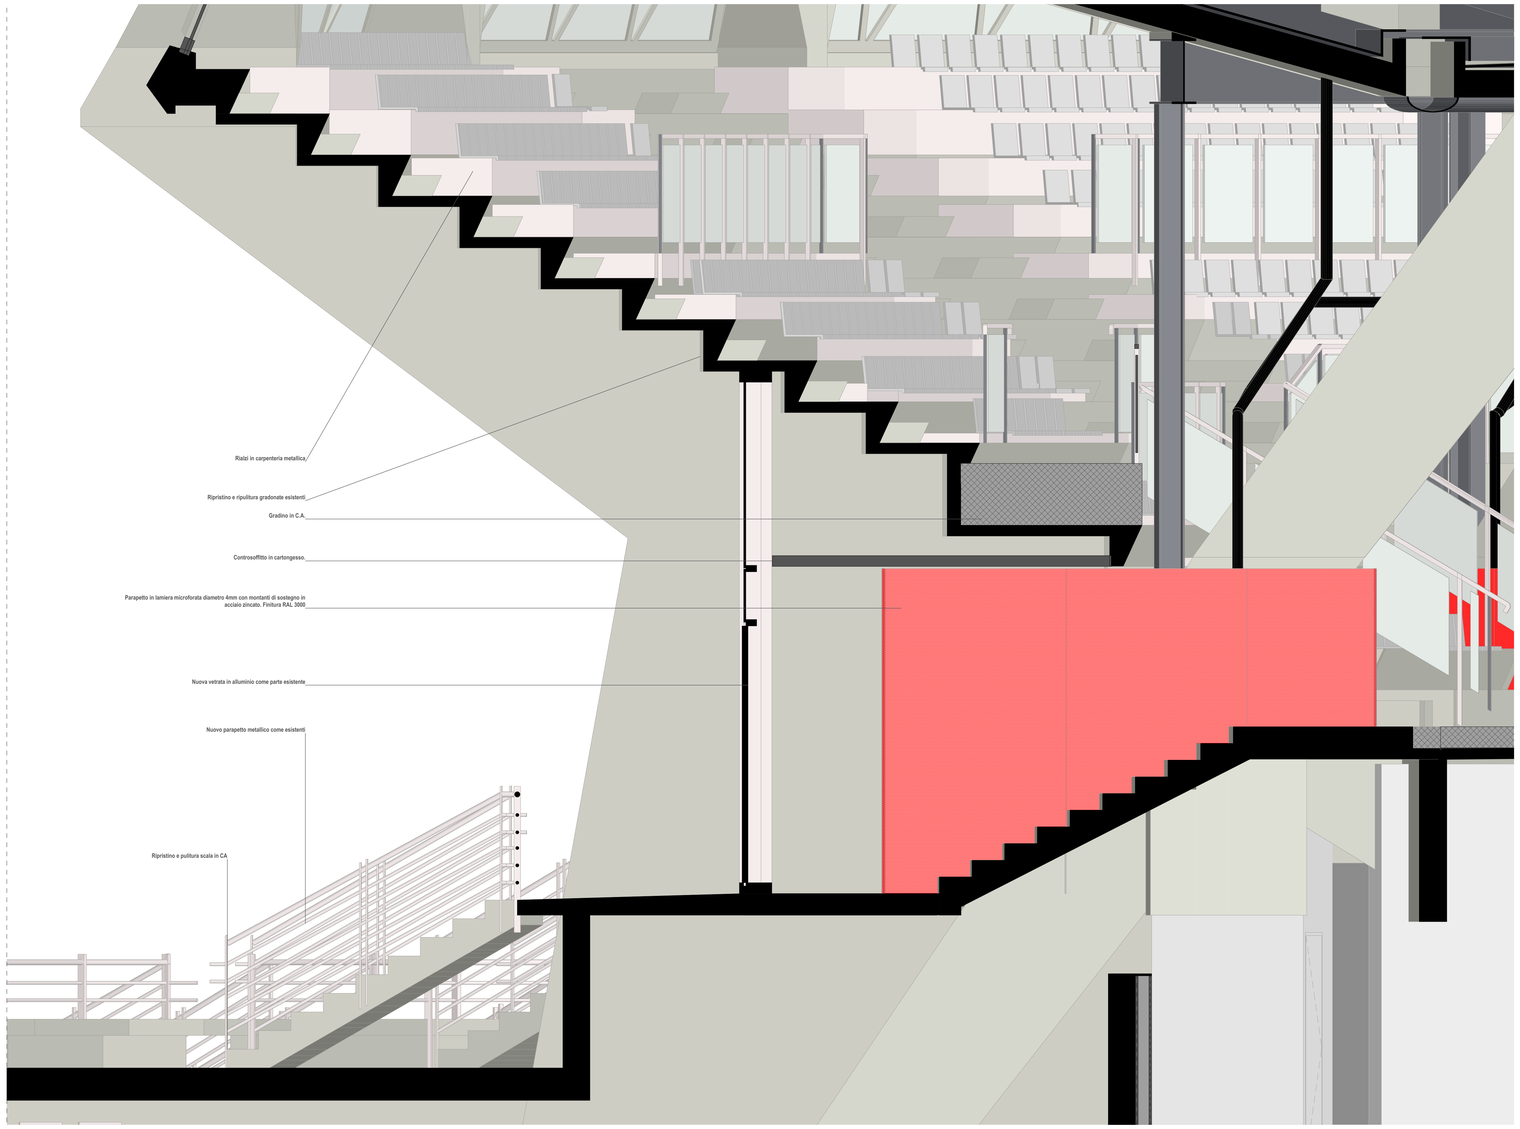

D02 Dettaglio 1:20

PROGETTO DEFINITIVO

PROGETTO ARCHITETTONICO

PROGETTISTA ARCHITETTONICO
Arch. Elena Brusa Pasquè
Studio Associato Brusa Pasquè
via Rainoldi 27 - 21100 Varese (VA)
tel: 0332 236317 mail: info@brusapasque.it

ORDINE DEGLI ARCHITETTI PIANIFICATORI PAESAGGISTI E CONSERVATORI DELLA PROVINCIA DI VARESE
Elena Brusa Pasquè
573

ING. STRUTTURISTA
Ing. Riccardo Aceti
Studio Aceti - ingegneria strutturale
via Pasubio 26, 21100 Varese (VA)

ORDINE DEGLI INGEGNERI DELLA PROVINCIA DI VARESE
Dott. Ing. RICCARDO ACETI n° 2197

PROGETTISTA IMPIANTI
SEINGIM - engineering & management
Via Angelo Scarsellini, 14, - 20161 Milano (MI)

ORDINE DEGLI INGEGNERI PROVINCIA DI MILANO
N. 4347

COMMITTENTE

Pallacanestro Varese
Piazzale Gramsci c/o Energxenia Arena
(Gestore del Palazzetto "Lino Oldrini" di Varese di proprietà comunale)

LUOGO OGGETTO DI INTERVENTO:

RIQUALIFICAZIONE E COMPLETAMENTO PALAZZETTO DELLO SPORT E REALIZZAZIONE DEL MUSEO DEL BASKET
Palazzetto dello Sport, Piazza Antonio Gramsci, Varese

CUP: B37H21001160002

TIPOLOGIA DI INTERVENTO

RISTRUTTURAZIONE EDILIZIA

REV.	DATA	DESCRIZIONE	DISEGNATO	VERIFICATO	APPROVATO
1	05/10/2021	PROGETTO DEFINITIVO	MZ	EBP	EBP
0	15/07/2021	PROGETTO DEFINITIVO	MZ	EBP	EBP

NOME FILE	
DATA DI STAMPA	
STILE DI STAMPA	
NOME LAYOUT	

TITOLO

SDP **PROSPETTO NORD-EST - DETTAGLI**

SCALA

1:100, 1:20

TAVOLA

NE - SDP - 06