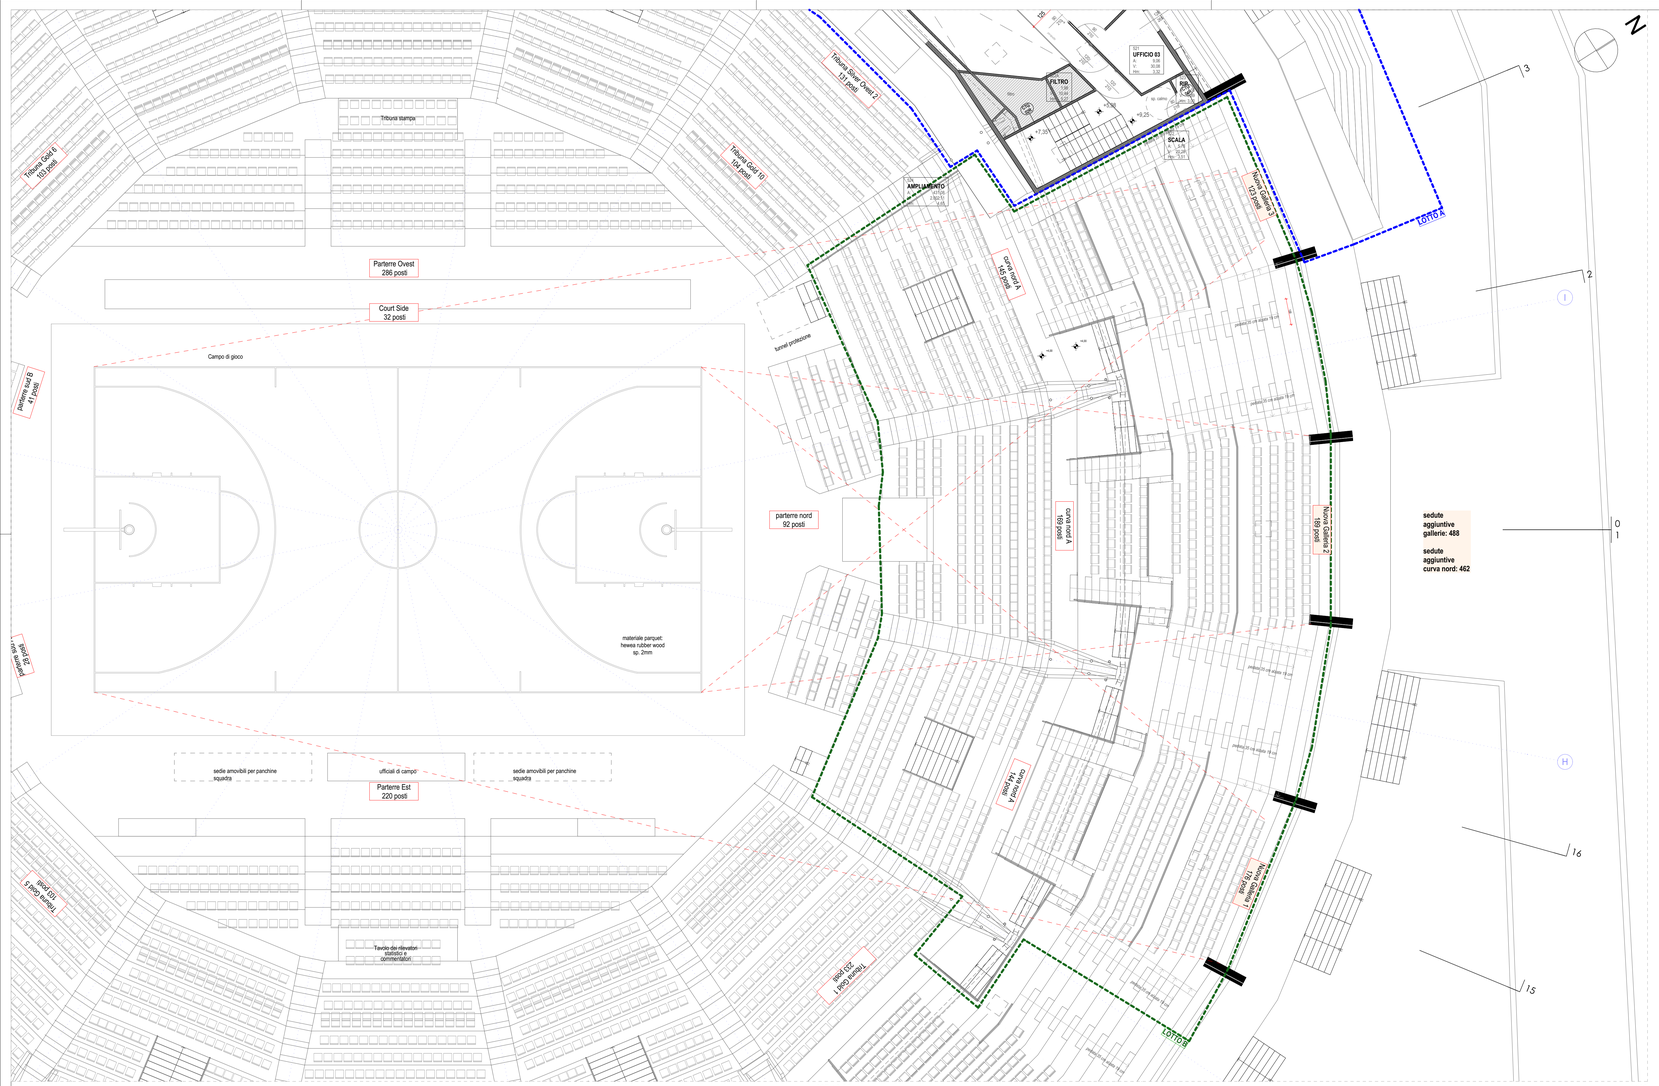

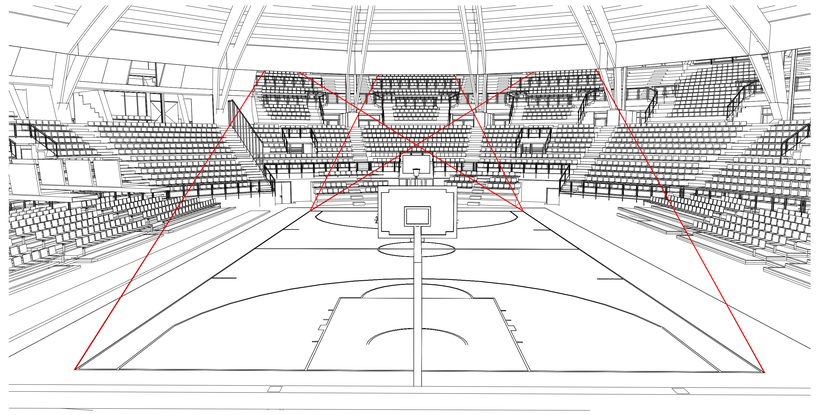

3D visibilità 1:78,67

NORME CONI PER L'IMPIANTISTICA SPORTIVA 6 5 2008 DELIBERA 149

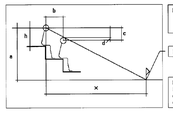

Formula per la verifica della visibilità:

$$x = b \cdot \frac{a}{d} - e$$

Limite più vicino del campo di gioco

h = m 0,80
Il valore minimo del parametro d è definito dalla normativa vigente. Il valore preferibile è di m 0,12.

UNI EN 13200-1 2019 pag 21

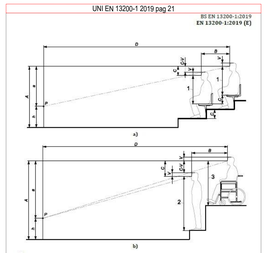

Key:
A height of eyes
B distance from one spectator to the spectator behind
C dimension of the riser of the step
h height of point of interest P (see Annex C)
D horizontal distance between spectator's eyes situated at height A and nearest point P of focus
P nearest point of focus along the line of sight
V vertical distance from eyes of a spectator to the top of the head(90 mm (minimum)) 110 mm (recommended).
C-V should be measured from the top of the head of the person sitting in the front row to the eye level of the person sitting in the row behind
a A- h (difference between height of eyes and height of point of interest)
1 distance from the eyes of a seating spectator and his place of rest: 800 mm
2 distance from the eyes of a spectator and the tread: 1 600 mm
3 distance from the eyes of a spectator in wheelchair and his plane: 1 150 mm

h = 500mm (pallacanestro)
come da norma UNI EN 13200-1 2019 annex C

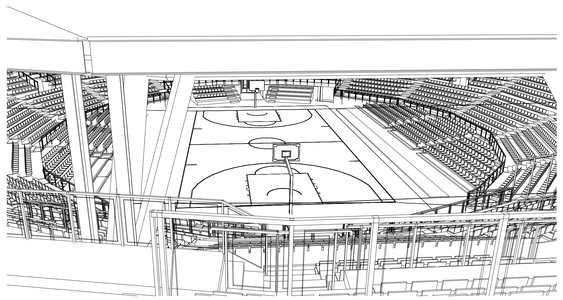

3D visibilità 2 1:100

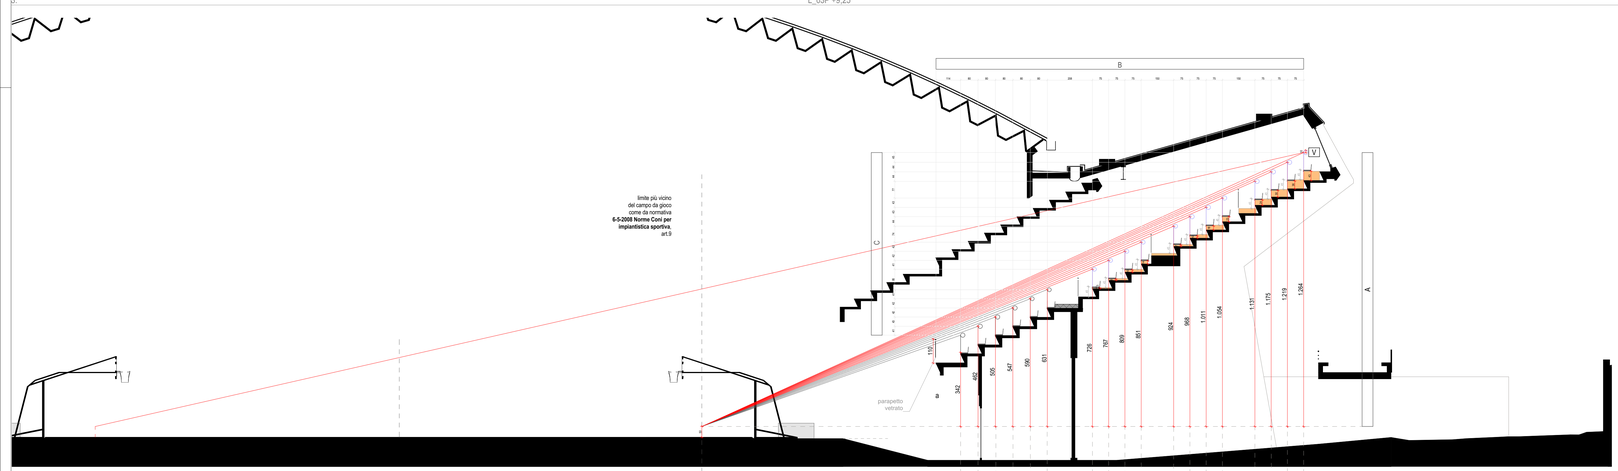

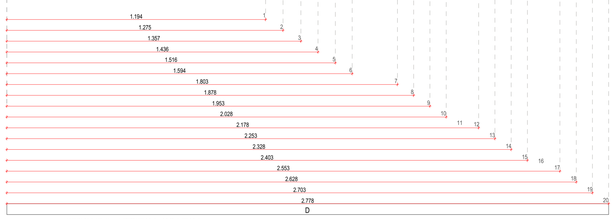

SEZIONE 0 - VERIFICA GRAFICA 1:100

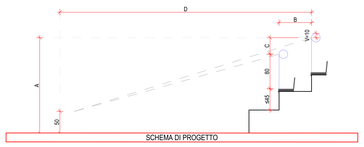

SCHEMA DI PROGETTO

Verifica Analitico Curva di Visibilità							
Gradinata in ampliamento	A (cm)	B (cm)	C (cm)	V (cm)	D= (A*B)/ (C-V) (cm)	x' (da rilievo)(cm)	Verifica
1	342	80	43	10	829	1194	TRUE
2	462	80	41	10	1.192	1275	TRUE
3	507	80	43	10	1.229	1357	TRUE
4	547	80	42	10	1.368	1436	TRUE
5	590	80	42	10	1.475	1.516	TRUE
6	632	80	42	10	1.580	1.594	TRUE
7	726	208	94	10	1.798	1.803	TRUE
8	767	75	41	10	1.856	1.878	TRUE
9	809	75	42	10	1.896	1.953	TRUE
10	851	75	42	10	1.995	2.028	TRUE
11		75	38	10	0	2.105	
12	924	150	74	10	2.166	2.178	TRUE
13	968	75	44	10	2.135	2.178	TRUE
14	1.011	75	43	10	2.298	2.328	TRUE
15	1.054	75	43	10	2.395	2.403	TRUE
16		75	38	10	0	2.478	
17	1.131	150	77	10	2.532	2.553	TRUE
18	1.175	75	44	10	2.592	2.628	TRUE
19	1.219	75	44	10	2.689	2.703	TRUE
20	1.264	75	45	10	2.709	2778	TRUE

verifica curva di visibilità_S0 1:1

PROGETTO DEFINITIVO

PROGETTO ARCHITETTONICO

PROGETTISTA ARCHITETTONICO
Arch. Elena Brusa Pasquè
Studio Associato Brusa Pasquè
via Rainoldi 27 - 21100 Varese (VA)
tel: 0332 236317 mail: info@brusapasque.it

ORDINE DEGLI ARCHITETTI PIANIFICATORI PAESAGGISTI E CONSERVATORI DELLA PROVINCIA DI VARESE
Arch. Elena Brusa Pasquè
Sez. A 573

ING. STRUTTURISTA
Ing. Riccardo Aceti
Studio Aceti - ingegneria strutturale
via Pasubio 26, 21100 Varese (VA)

ORDINE DEGLI INGEGNERI DELLA PROVINCIA DI VARESE
Dott. Ing. RICCARDO ACETI
n° 2797

PROGETTISTA IMPIANTI
SEINGIM - engineering & management
Via Angelo Scarsellini, 14, - 20161 Milano (MI)

ORDINE INGEGNERI PROVINCIA DI MILANO
N. 4347

COMMITTENTE

Pallacanestro Varese
Piazzale Gramsci c/o Enervxenia Arena
(Gestore del Palazzetto "Lino Oldrini" di Varese di proprietà comunale)

LUOGO OGGETTO DI INTERVENTO:

RIQUALIFICAZIONE E COMPLETAMENTO PALAZZETTO DELLO SPORT E REALIZZAZIONE DEL MUSEO DEL BASKET
Palazzetto dello Sport, Piazza Antonio Gramsci, Varese

CUP: B37H21001160002

TIPOLOGIA DI INTERVENTO

RISTRUTTURAZIONE EDILIZIA

REV.	DATA	DESCRIZIONE	DISEGNATO	VERIFICATO	APPROVATO
1	05/10/2021	PROGETTO DEFINITIVO	MZ	EBP	EBP
0	15/07/2021	PROGETTO DEFINITIVO	MZ	EBP	EBP

NOME FILE	
DATA DI STAMPA	
STILE DI STAMPA	
NOME LAYOUT	

TITOLO
SDP CURVE VISIBILITA

SCALA
1:100

TAVOLA
NE - SDP - 07