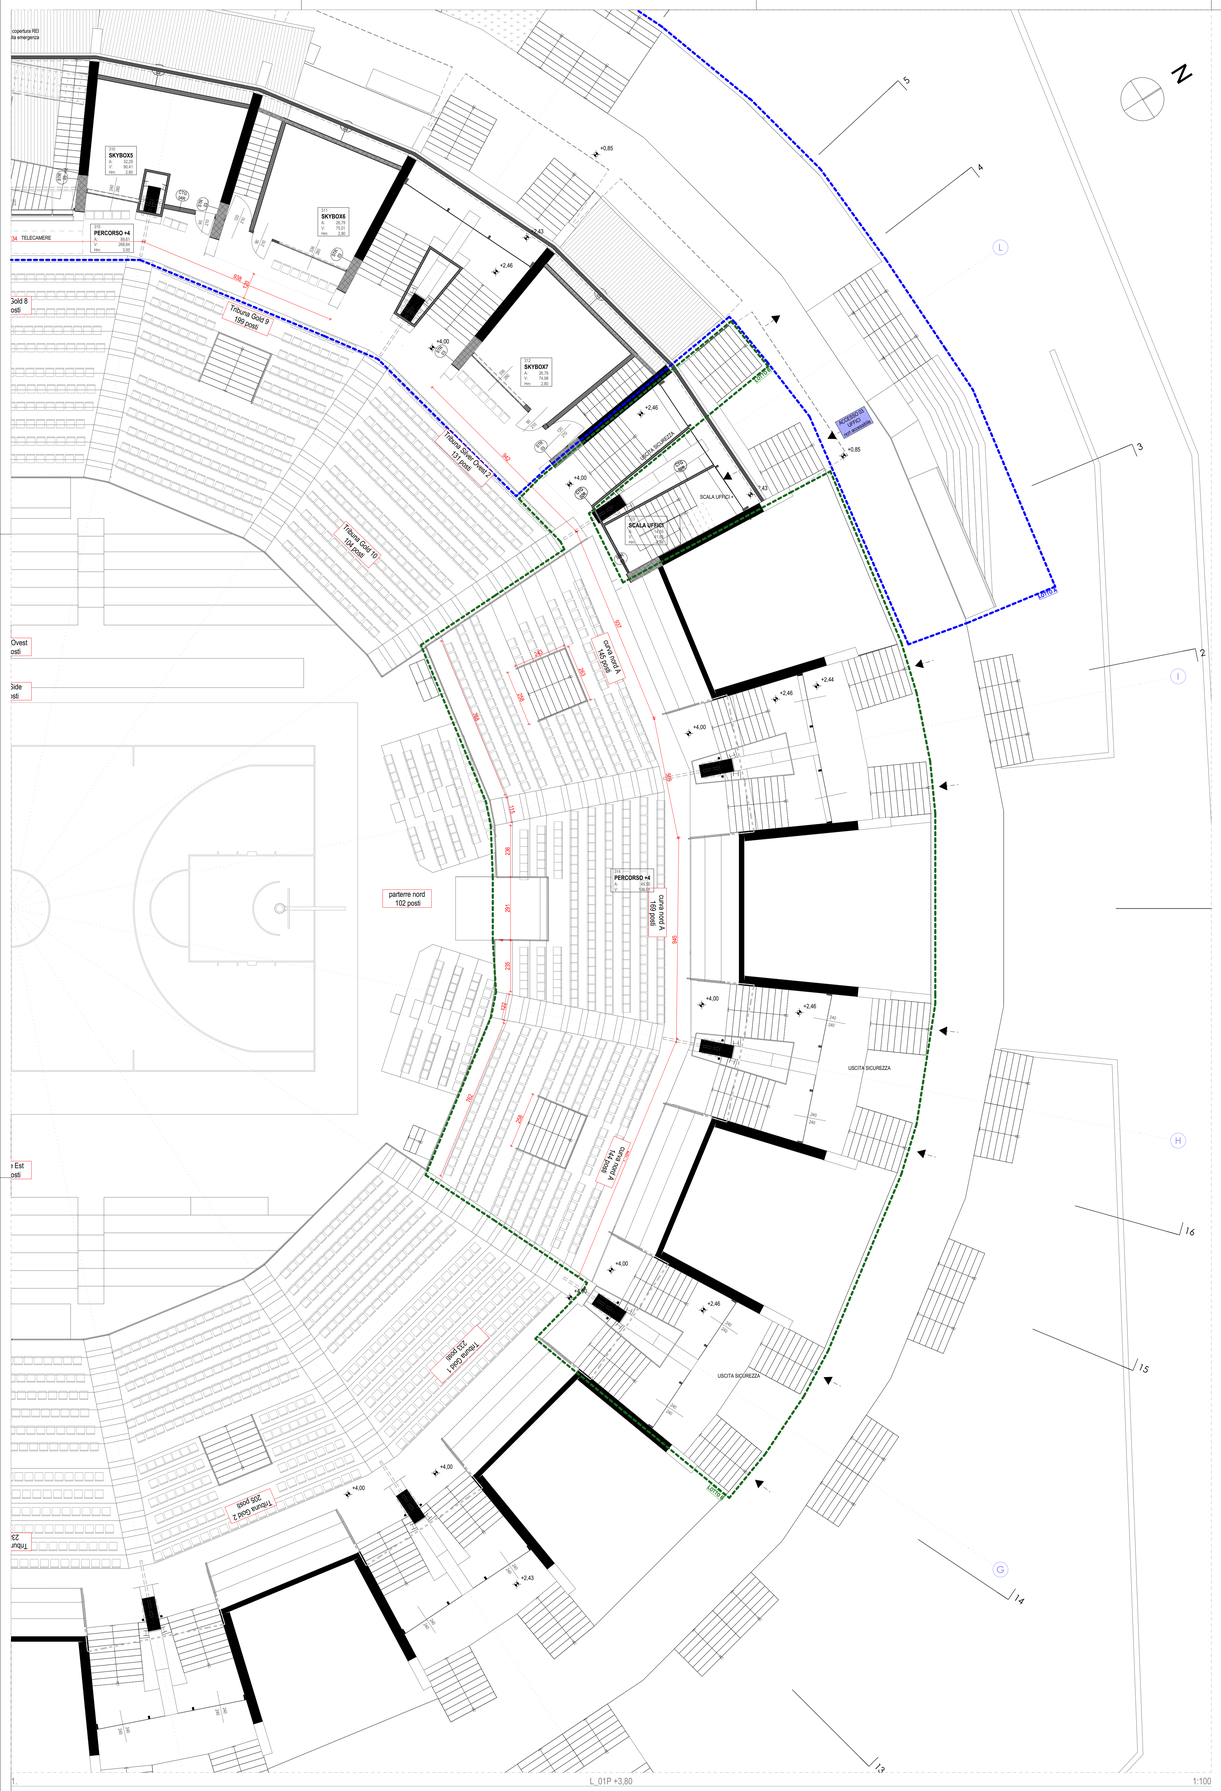

L_01P +3,80 1:100

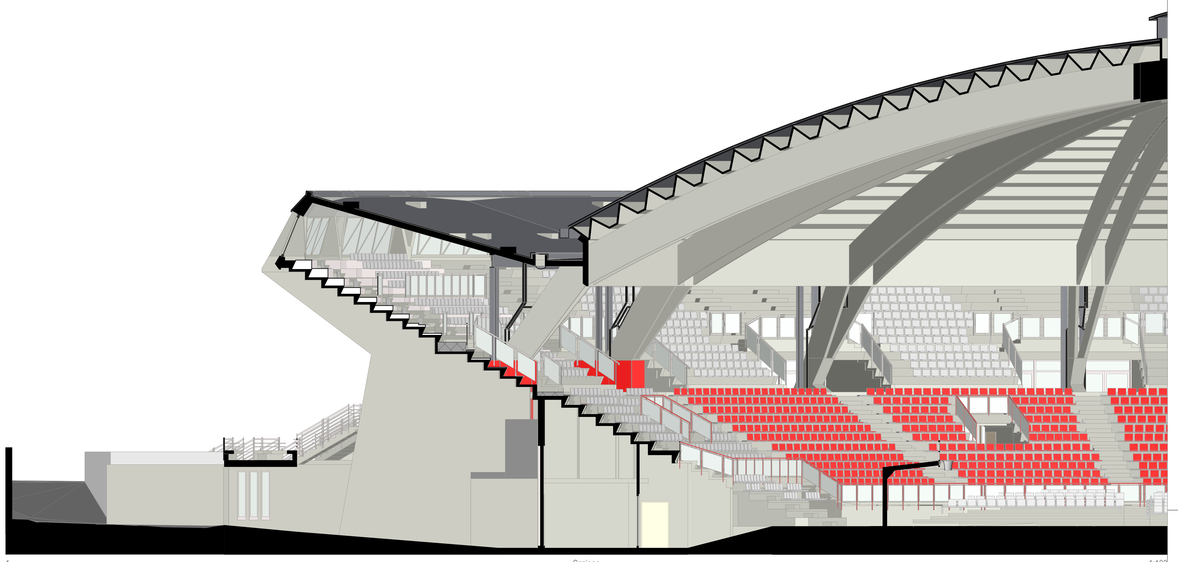

1 Sezione 1:100

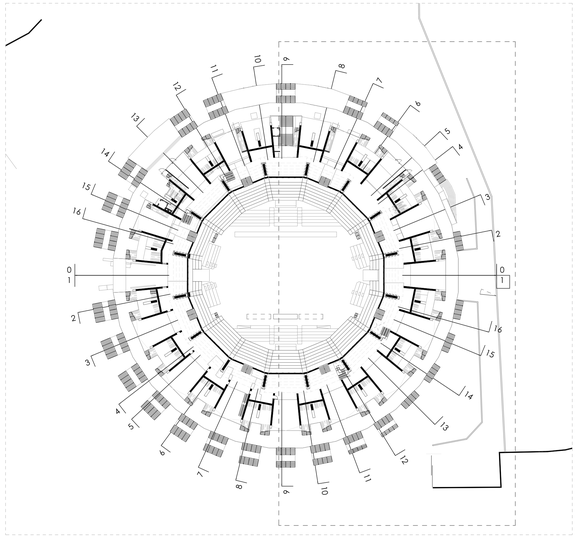

KEYPLAN SDP

LEGENDA MURATURE

CTG 01 1 cm. Lastra cartongesso tipo standard 1 cm. Lastra cartongesso tipo standard 1 cm. Aria / Ventilazione 4 cm. Pannelli di lana di roccia 1 cm. Lastra cartongesso tipo standard 1 cm. Lastra cartongesso tipo standard	CTG 04R 1 cm. Lastra cartongesso resistente al fuoco 1 cm. Lastra cartongesso resistente al fuoco 4 cm. Pannelli di lana di roccia 1 cm. Lastra cartongesso resistente al fuoco 1 cm. Lastra cartongesso resistente al fuoco
CTG 09 1 cm. Lastra cartongesso resistente al fuoco 1 cm. Lastra cartongesso resistente al fuoco 1 cm. Aria / ventilazione 4 cm. Pannelli di lana di roccia 1 cm. Lastra cartongesso resistente al fuoco 1 cm. Lastra cartongesso resistente al fuoco	CTG 09A 1 cm. Lastra cartongesso tipo standard 1 cm. Lastra cartongesso ad elevata resistenza 4 cm. Pannelli di lana di roccia 1 cm. Lastra cartongesso resistente all'acqua 1 cm. Lastra cartongesso resistente all'acqua
CTG 01 1 cm. Lastra cartongesso tipo standard 1 cm. Lastra cartongesso ad elevata resistenza 4 cm. Pannelli di lana di roccia 6 cm. Pannelli di lana di roccia 1 cm. Lastra cartongesso resistente all'acqua 1 cm. Lastra cartongesso resistente all'acqua	STR 03 20 cm. CLS per travi plastri scale C28/30 Rivestimento in lamiera forata

LEGENDA SIMBOLOGIA

- ETICHETTA MURATURE
- C7 N. SEZIONE
- QUOTA PAVIMENTO SDP +0.00
- NON ACCESSIBILE
- LOTTO A — MUSEO - UFFICI BAR RISTORO
- LOTTO B — AMPLIAMENTO PALAZZETTO

CONVENZIONE DISEGNO

ESISTENTE | PROGETTO

LEGENDA SOLAI

SOL 01 / CA 5 cm. Isolamento - EPS 30 cm. Caseiforme solaio - EPS: travetti CA passo 50 5 cm. CLS per travi plastri scale C28/30	COP 01 20 cm. Isolamento - EPS 4 cm. Guaina impermeabile - alta riflettanza solare COP / SP 20 cm. CLS prefabbricato solaio 1 cm. Alluminio
SOL 02 / CA 5 cm. Isolamento - EPS 30 cm. Caseiforme solaio - EPS: travetti CA passo 50 5 cm. CLS per travi plastri scale C28/30	COP 02 / CARP 2 cm. Pannelli truciolato 12 cm. Isolamento - EPS 4 cm. Aria / Ventilazione 1 cm. Alluminio

PROGETTO DEFINITIVO

PROGETTO ARCHITETTONICO

PROGETTISTA ARCHITETTONICO
Arch. Elena Brusa Pasquè
Studio Associato Brusa Pasquè
via Rainoldi 27 - 21100 Varese (VA)
tel: 0332 236317 mail: info@brusapasque.it

ORDINE DEGLI ARCHITETTI PIANIFICATORI PAESAGGISTI E CONSERVATORI DELLA PROVINCIA DI VARESE
Elena Brusa Pasquè
Architetto
573
SEZIONE A

ING. STRUTTURISTA
Ing. Riccardo Aceti
Studio Aceti - ingegneria strutturale
via Pasubio 26, 21100 Varese (VA)

ORDINE DEGLI INGEGNERI DELLA PROVINCIA DI VARESE
Dott. Ing. RICCARDO ACETI n° 2197
Settore A - Civile e Ambientale

PROGETTISTA IMPIANTI
SEINGIM - engineering & management
Via Angelo Scarsellini, 14, - 20161 Milano (MI)

ORDINE DEGLI INGEGNERI DELLA PROVINCIA DI MILANO
N. 4347

COMMITTENTE

Pallacanestro Varese
Piazzale Gramsci c/o Enerxenia Arena
(Gestore del Palazzetto "Lino Oldrini" di Varese di proprietà comunale)

LUOGO OGGETTO DI INTERVENTO:

RIQUALIFICAZIONE E COMPLETAMENTO PALAZZETTO DELLO SPORT E REALIZZAZIONE DEL MUSEO DEL BASKET
Palazzetto dello Sport, Piazza Antonio Gramsci, Varese

CUP: B37H21001160002

TIPOLOGIA DI INTERVENTO

RISTRUTTURAZIONE EDILIZIA

REV.	DATA	DESCRIZIONE	DISEGNATO	VERIFICATO	APPROVATO
1	05/10/2021	PROGETTO DEFINITIVO	MZ	EBP	EBP
0	15/07/2021	PROGETTO DEFINITIVO	MZ	EBP	EBP

NOME FILE	
DATA DI STAMPA	
STILE DI STAMPA	
NOME LAYOUT	

TITOLO

SDP **PIANTA | PIANO +3,80**

SCALA

1:100

TAVOLA

NE - SDP - 03